

A NEW RESIDENCE FOR:

MIDTERM HOUSE



HALF SIZE

SHEET INDEX	
NUMBER	SHEET NAME
1G	COVER SHEET
A0	BASEMENT PLAN
A1	FIRST FLOOR PLAN
A2	SECOND FLOOR PLAN
A3	ROOF PLAN
A4	SOUTH EXTERIOR ELEVATION
A5	EXTERIOR ELEVATIONS
A6	BUILDING SECTION
A7	WALL SECTION
S0	FOUNDATION PLAN

SQUARE FOOTAGE	
NAME	AREA
MAIN LEVEL GROSS SF	1553 SF
GARAGE GROSS SF	698 SF
BASEMENT GROSS SF	151 SF
SECOND LEVEL GROSS SF	777 SF

 AUTODESK®

www.autodesk.com/revit

Consultant
Address
Address
Phone
Fax
e-mail

PARKER HICKS
MIDTERM HOUSE
COVER SHEET

Project number	2022-00
Date	11/30/2022
Drawn by	PARKER HICKS
Checked by	CHECKED

1G

3/8" - 1' 0"



www.autodesk.com/revit

Consultant
Address
Address
Phone
Fax
e-mail

WINDOW SCHEDULE

WINDOW SCHEDULE					
MARK	WINDOW SIZE		COUNT	WINDOW TYPE	FRAME MATERIAL
	WIDTH	HEIGHT			
B	4' - 9"	6' - 0"	11	Window-Casement-Double	METAL CLAD WOOD WINDOW
C	2' - 0"	2' - 0"	4	Fixed with Trim	VINYL WINDOW
D	2' - 0"	6' - 0"	2	Fixed with Trim	METAL CLAD WOOD WINDOW
E	3' - 0"	6' - 0"	3	Fixed with Trim	VINYL WINDOW
F	4' - 9"	9' - 0"	2	Window-Casement-Double	METAL CLAD WOOD WINDOW

DOOR SCHEDULE

DOOR SCHEDULE					
DOOR TYPE	WIDTH	HEIGHT	COUNT	COMMENTS	FUNCTION
1	3' - 0"	7' - 0"	3		Exterior
2	1' - 0"	7' - 2"	2		Exterior
3	6' - 0"	8' - 0"	1		Exterior
4	2' - 2"	6' - 8"	2		Interior
5	2' - 0"	7' - 0"	2		Interior
6	2' - 8"	6' - 8"	1		Interior
7	3' - 0"	7' - 0"	1		Interior
8	2' - 6"	6' - 8"	2		Interior
9	2' - 4"	6' - 8"	4		Interior
10	3' - 0"	6' - 8"	1		Exterior
11	8' - 0"	7' - 0"	2		Exterior
74	0' - 0"	0' - 0"	2		Interior
77	0' - 0"	0' - 0"	1		Interior

This architectural floor plan illustrates a two-story structure with various rooms and dimensions. The overall width is 39' - 6" and the overall depth is 29' - 8". Key features include:

- Shop/Storage:** 215 SF, located on the upper level.
- Mudhall:** 152 SF, located on the lower level, featuring an "UP" access point.
- GARAGE:** 419 SF, located on the lower level, featuring two "11" access points.
- Staircases:** Two sets of stairs are shown, one leading up from the lower level to the mudhall, and another leading down from the mudhall to the basement.
- Dimensions:** The plan includes numerous dimensions for rooms and hallways, such as 12' - 5", 21' - 9", 29' - 8", 7' - 11", 10' - 1", 4' - 1 1/2", 4' - 9", 5' - 10 1/2", 9' - 4", and 5' - 4".
- Labels:** Labels include "UP", "B", and room names like "SHOP/STORAGE" and "MUDHALL".
- Notes:** A note at the bottom left indicates "1/4" = 1'-0".

1 BASEMENT
1/4" = 1'-0"

PARKER HICKS
MIDTERM HOUSE
BASEMENT PLAN

Project number	2022-001
Date	11/30/2022
Drawn by	PARKER HICKS
Checked by	CHECKER

A0

1/4" = 1'-0"



www.autodesk.com/revit

Consultant
Address
Address
Phone
Fax
e-mail

WINDOW SCHEDULE					
MARK	WINDOW SIZE		COUNT	WINDOW TYPE	FRAME MATERIAL
	WIDTH	HEIGHT			
B	4' - 9"	6' - 0"	11	Window-Casement-Double	METAL CLAD WOOD WINDOW
C	2' - 0"	2' - 0"	4	Fixed with Trim	VINYL WINDOW
D	2' - 0"	6' - 0"	2	Fixed with Trim	METAL CLAD WOOD WINDOW
E	3' - 0"	6' - 0"	3	Fixed with Trim	VINYL WINDOW
F	4' - 9"	9' - 0"	2	Window-Casement-Double	METAL CLAD WOOD WINDOW


DOOR SCHEDULE					
DOOR TYPE	WIDTH	HEIGHT	COUNT	COMMENTS	FUNCTION
1	3' - 0"	7' - 0"	3		Exterior
2	1' - 0"	7' - 2"	2		Exterior
3	6' - 0"	8' - 0"	1		Exterior
4	2' - 2"	6' - 8"	2		Interior
5	2' - 0"	7' - 0"	2		Interior
6	2' - 8"	6' - 8"	1		Interior
7	3' - 0"	7' - 0"	1		Interior
8	2' - 6"	6' - 8"	2		Interior
9	2' - 4"	6' - 8"	4		Interior
10	3' - 0"	6' - 8"	1		Exterior
11	8' - 0"	7' - 0"	2		Exterior
74	0' - 0"	0' - 0"	2		Interior
77	0' - 0"	0' - 0"	1		Interior

PARKER HICKS
MIDTERM HOUSE
FIRST FLOOR PLAN

Object number	2022-001
Date	11/30/2022
Borrowed by	PARKER HICKS
Checked by	CHECKER

A1

1/4" = 1'-0"

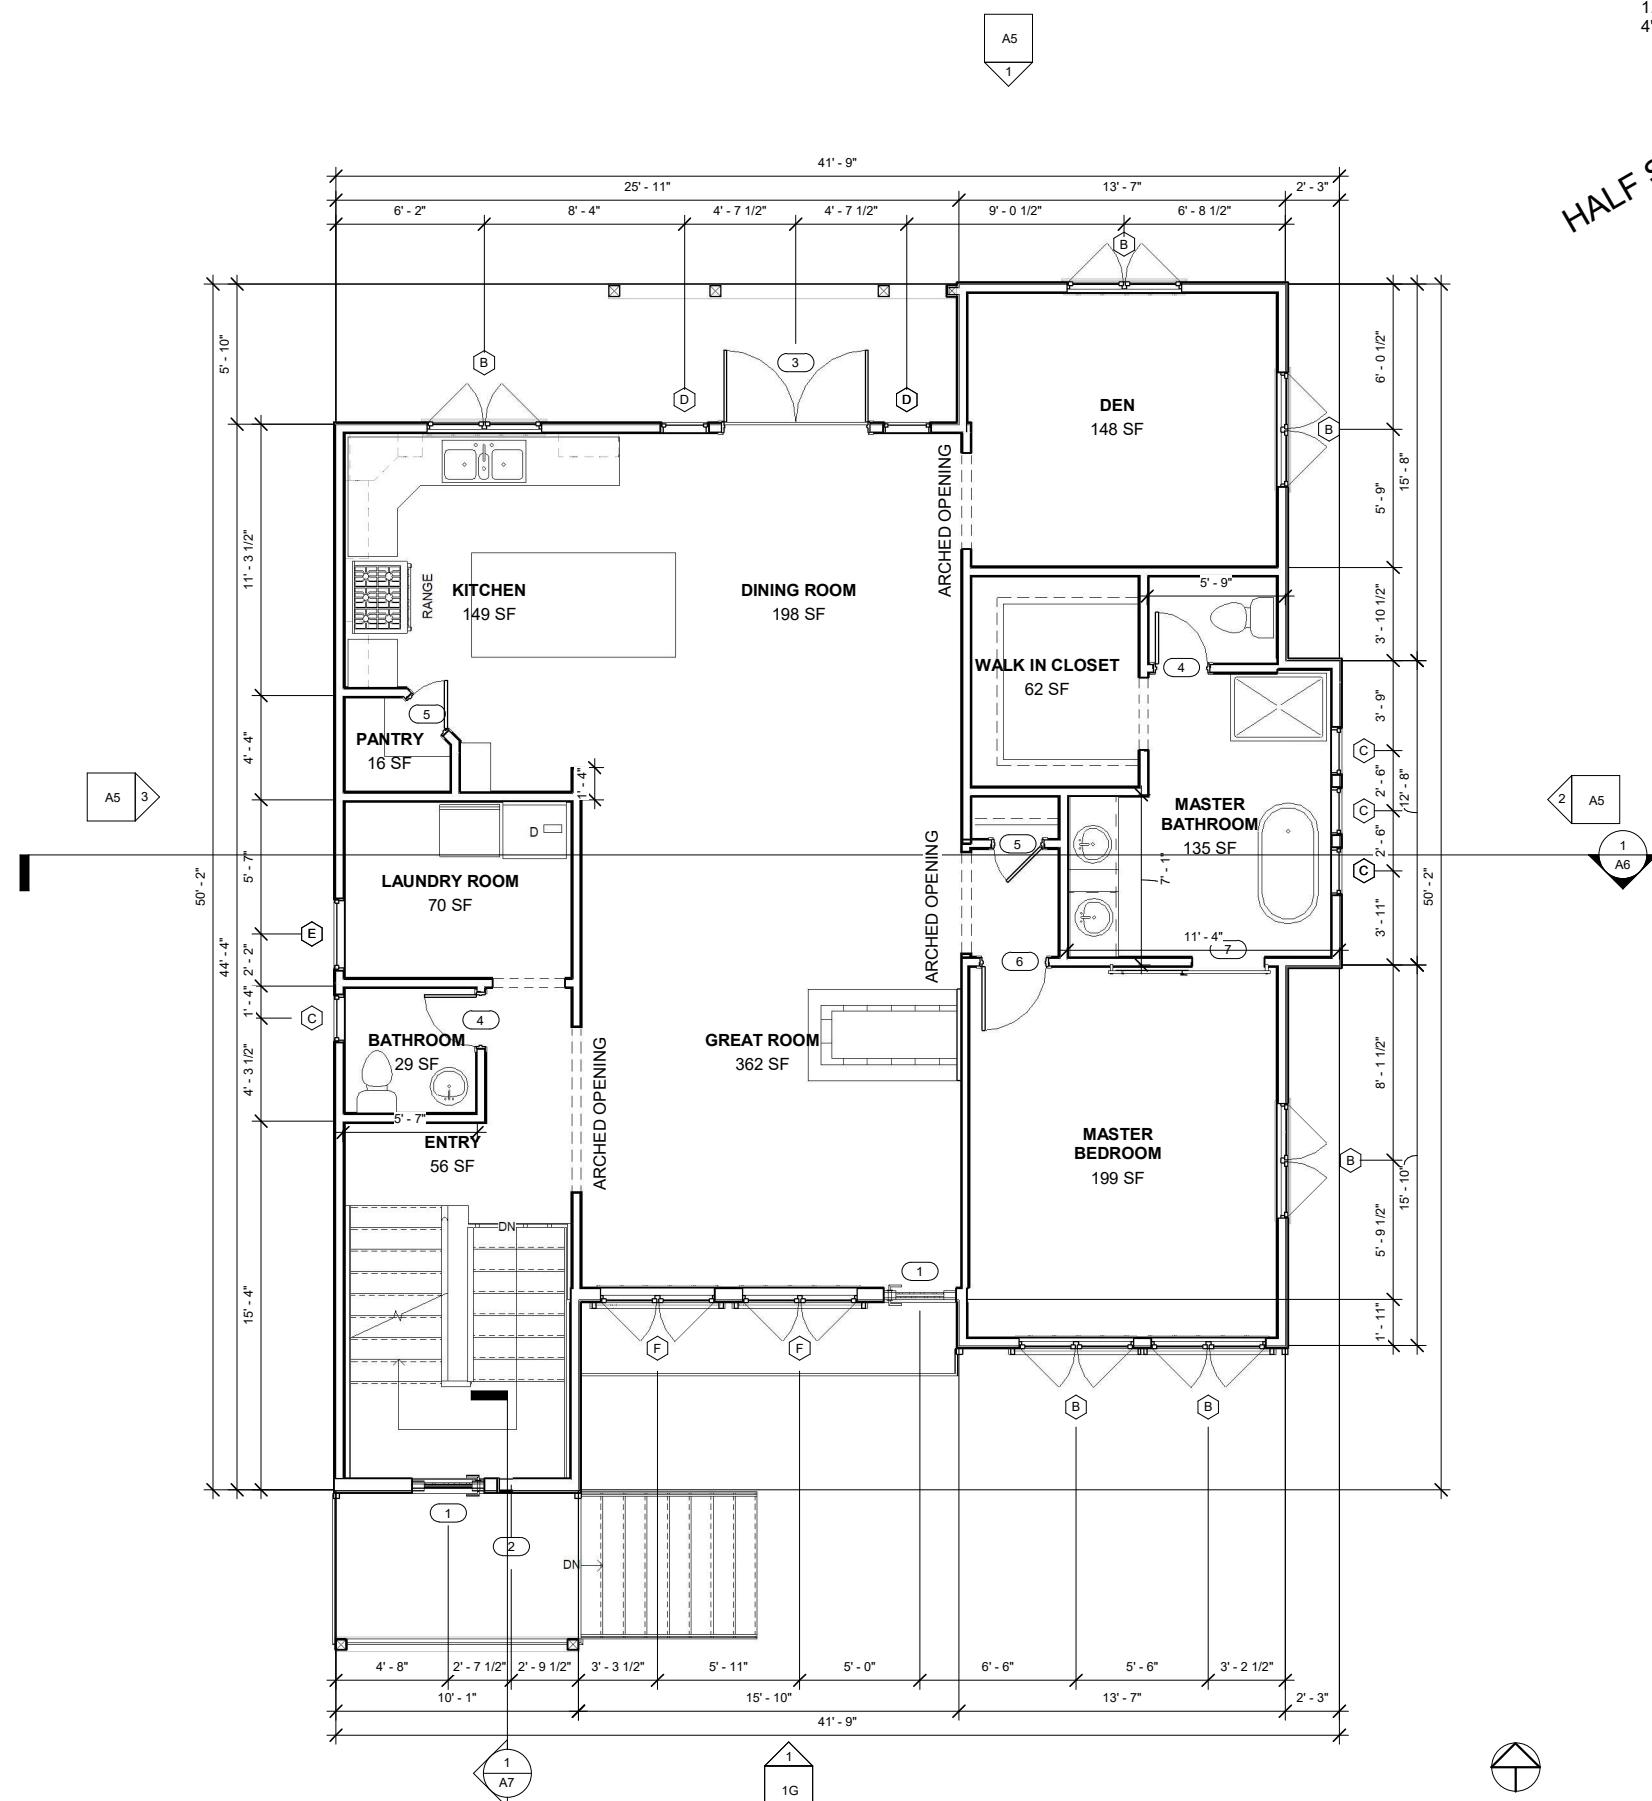

1 FIRST FLOOR
1/4" = 1'-0"



www.autodesk.com/revit

Consultant
Address
Address
Phone
Fax
e-mail

WINDOW SCHEDULE					
MARK	WINDOW SIZE		COUNT	WINDOW TYPE	FRAME MATERIAL
	WIDTH	HEIGHT			
B	4' - 9"	6' - 0"	11	Window-Casement-Double	METAL CLAD WOOD WINDOW
C	2' - 0"	2' - 0"	4	Fixed with Trim	VINYL WINDOW
D	2' - 0"	6' - 0"	2	Fixed with Trim	METAL CLAD WOOD WINDOW
E	3' - 0"	6' - 0"	3	Fixed with Trim	VINYL WINDOW
F	4' - 9"	9' - 0"	2	Window-Casement-Double	METAL CLAD WOOD WINDOW

DOOR SCHEDULE					
DOOR TYPE	WIDTH	HEIGHT	COUNT	COMMENTS	FUNCTION
1	3' - 0"	7' - 0"	3		Exterior
2	1' - 0"	7' - 2"	2		Exterior
3	6' - 0"	8' - 0"	1		Exterior
4	2' - 2"	6' - 8"	2		Interior
5	2' - 0"	7' - 0"	2		Interior
6	2' - 8"	6' - 8"	1		Interior
7	3' - 0"	7' - 0"	1		Interior
8	2' - 6"	6' - 8"	2		Interior
9	2' - 4"	6' - 8"	4		Interior
10	3' - 0"	6' - 8"	1		Exterior
11	8' - 0"	7' - 0"	2		Exterior
74	0' - 0"	0' - 0"	2		Interior
77	0' - 0"	0' - 0"	1		Interior

PARKER HICKS
MIDTERM HOUSE
SECOND FLOOR
PLAN

Project number	2022-00
Date	11/30/2022
Drawn by	PARKER HICKS
Checked by	CHECKER

A2

1/4" = 1'-0"

SECOND FLOOR

1/4" = 1'-0"

HALF SIZE

Rooms and Dimensions:

- BEDROOM** 152 SF (Dimensions: 8' - 6" x 18' - 9")
- CLOSET** 29 SF (Dimensions: 6' - 3" x 5' - 3")
- CLOSET** 32 SF (Dimensions: 6' - 11" x 5' - 8 1/2")
- BEDROOM** 162 SF (Dimensions: 14' - 8" x 11' - 7 1/2")
- PLAYROOM** 250 SF (Dimensions: 26' - 9" x 10' - 1")
- STORAGE** 30 SF (Dimensions: 5' - 5 3/8" x 6' - 2 7/8")
- BATHROOM** 68 SF (Dimensions: 10' - 1" x 14' - 11 3/8")

Other Features:

- Laundry chute** located in the Storage area.
- Stairs** leading down from the Playroom.
- Windows** indicated by dashed lines along the exterior walls.
- Doors** indicated by solid lines with door symbols.
- Labels A5, A6, A7, 1G, 1, B, C, D, E, F** placed around the perimeter and interior of the floor plan.



www.autodesk.com/revit

Consultant
Address
Address
Phone
Fax
e-mail

PARKER HICKS
MIDTERM HOUSE
ROOF PLAN


Project number	2022-001
Date	11/30/2022
Drawn by	PARKER HICKS
Checked by	CHECKER

A3

1/4" = 1'-0"

GENERAL NOTES:

1. ROOFING SYSTEM TO BE STANDING SEAM METAL ROOF UNLESS OTHERWISE NOTED.
2. ALL VENTS THROUGH ROOF TO BE INSTALLED ON THE BACKSIDE OF THE ROOF.

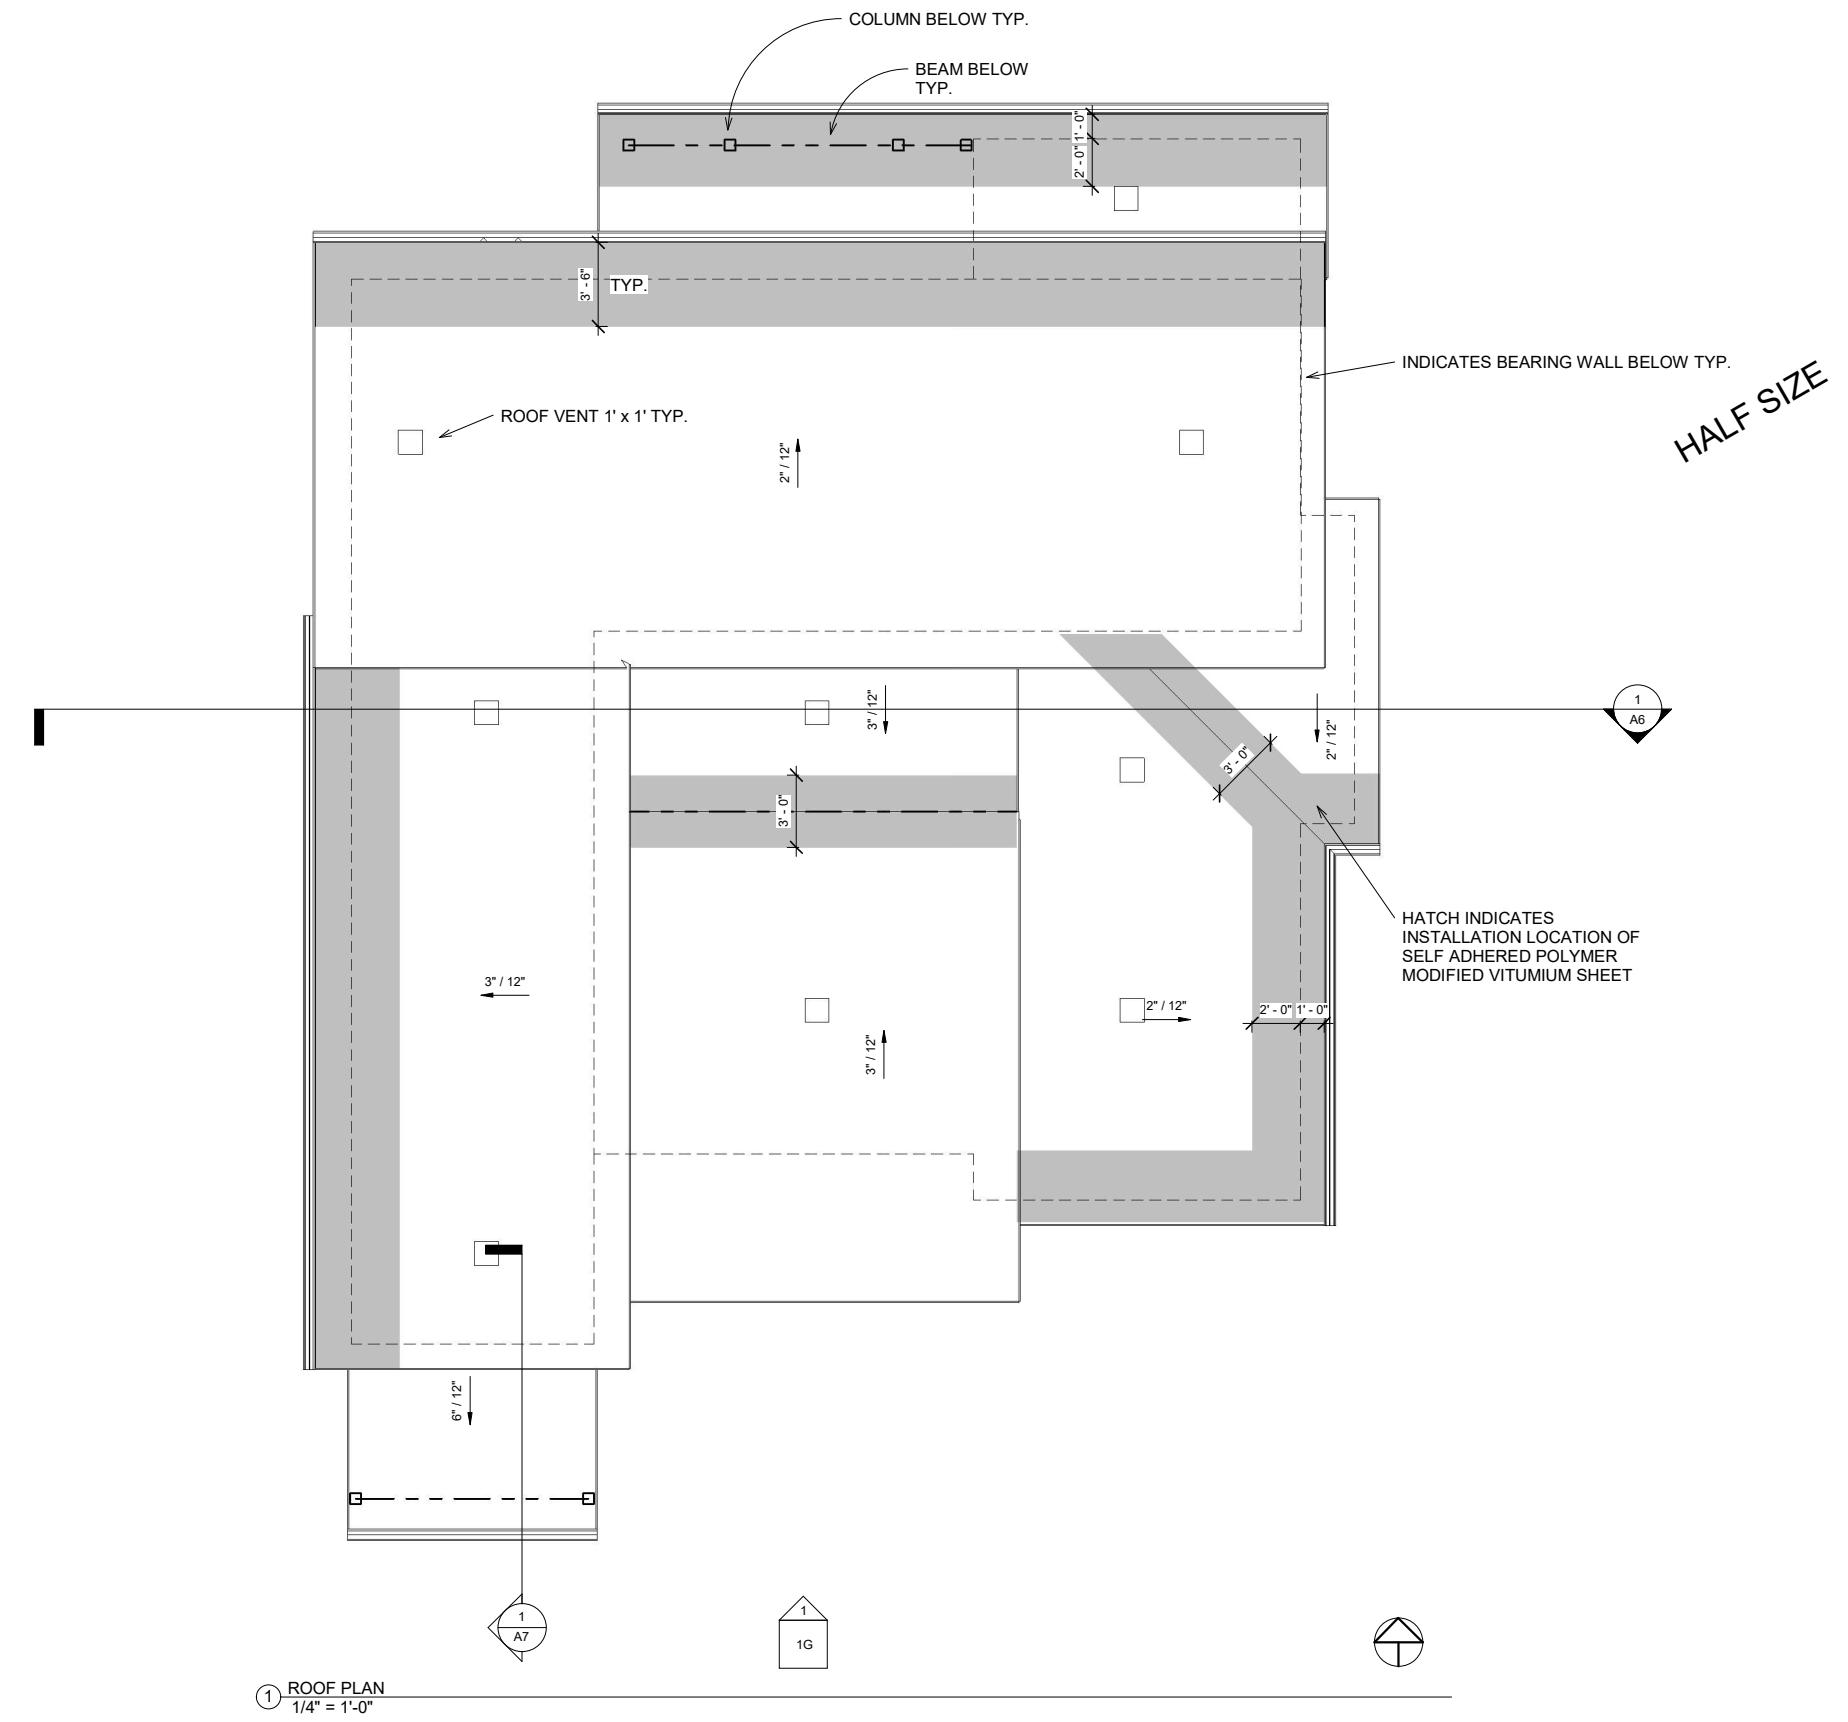



www.autodesk.com/revit

HALF SIZE



1 SOUTH EXTERIOR ELEVATION
3/8" = 1'-0"

PARKER HICKS
MIDTERM HOUSE
SOUTH EXTERIOR
ELEVATION

Project number	2022-00
Date	11/30/2022
Drawn by	PARKER HICKS
Checked by	CHECKER

A4

3/8" = 1'-0"



www.autodesk.com/revit

DASHED LINES INDICATED FOUNDATION/FOOTING TYP.

ROOF BEARING
18' - 0 5/8"

SECOND FLOOR
10' - 0 5/8"

T.O. WALL
9' - 0"

FIRST FLOOR
0' - 0"

T.O. FOUNDATION
-1' - 2 1/8"

T.O. FOOTING
-4' - 4 1/8"

B.O. FOOTING
-5' - 2 1/8"

BASEMENT
-9' - 10 1/8"

T.O. BASEMENT FOOTING
-10' - 2 1/8"

B.O. BASEMENT FOOTING
-11' - 0 1/8"

HALF SIZE

(3) WEST EXTERIOR ELEVATION
3/16" = 1'-0"

ROOF BEARING
18' - 0 5/8"

SECOND FLOOR
10' - 0 5/8"

T.O. WALL
9' - 0"

FIRST FLOOR
0' - 0"

T.O. FOUNDATION
-1' - 2 1/8"

T.O. FOOTING
-4' - 4 1/8"

B.O. FOOTING
-5' - 2 1/8"

BASEMENT
-9' - 10 1/8"

T.O. BASEMENTFOOTING
-10' - 2 1/8"

B.O. BASEMENTFOOTING
-11' - 0 1/8"

DASHED LINES
INDICATED
FOUNDATION/FOOTING
TYP.

(2) EAST EXTERIOR ELEVATION
2 1/4" = 1'-0"

ROOF BEARING
18'- 0 5/8"

SECOND FLOOR
T.O. WALL
9'- 0"

FIRST FLOOR
0'- 0"

T.O. FOUNDATION
-1' - 2 1/8"

T.O. FOOTING
-4' - 4 1/8"

B.O. FOOTING
-5' - 2 1/8"

BASEMENT
-9' - 10 1/8"

T.O. BASEMENT FOOTING
-10' - 2 1/8"

B.O. BASEMENT FOOTING
-11' - 0 1/8"

D LINES
TIED
TO
FOUNDATION/FOOTING
T.Y.P.

OUT
ENT

NORTH EXTERIOR ELEVATION


PARKER HICKS
MIDTERM HOUSE
EXTERIOR
ELEVATIONS

ELEVATIONS	
Project number	2022-001
Date	11/30/2022
Drawn by	PARKER HICKS
Checked by	CHECKER

A5

3/16" = 1'

HALF SIZE

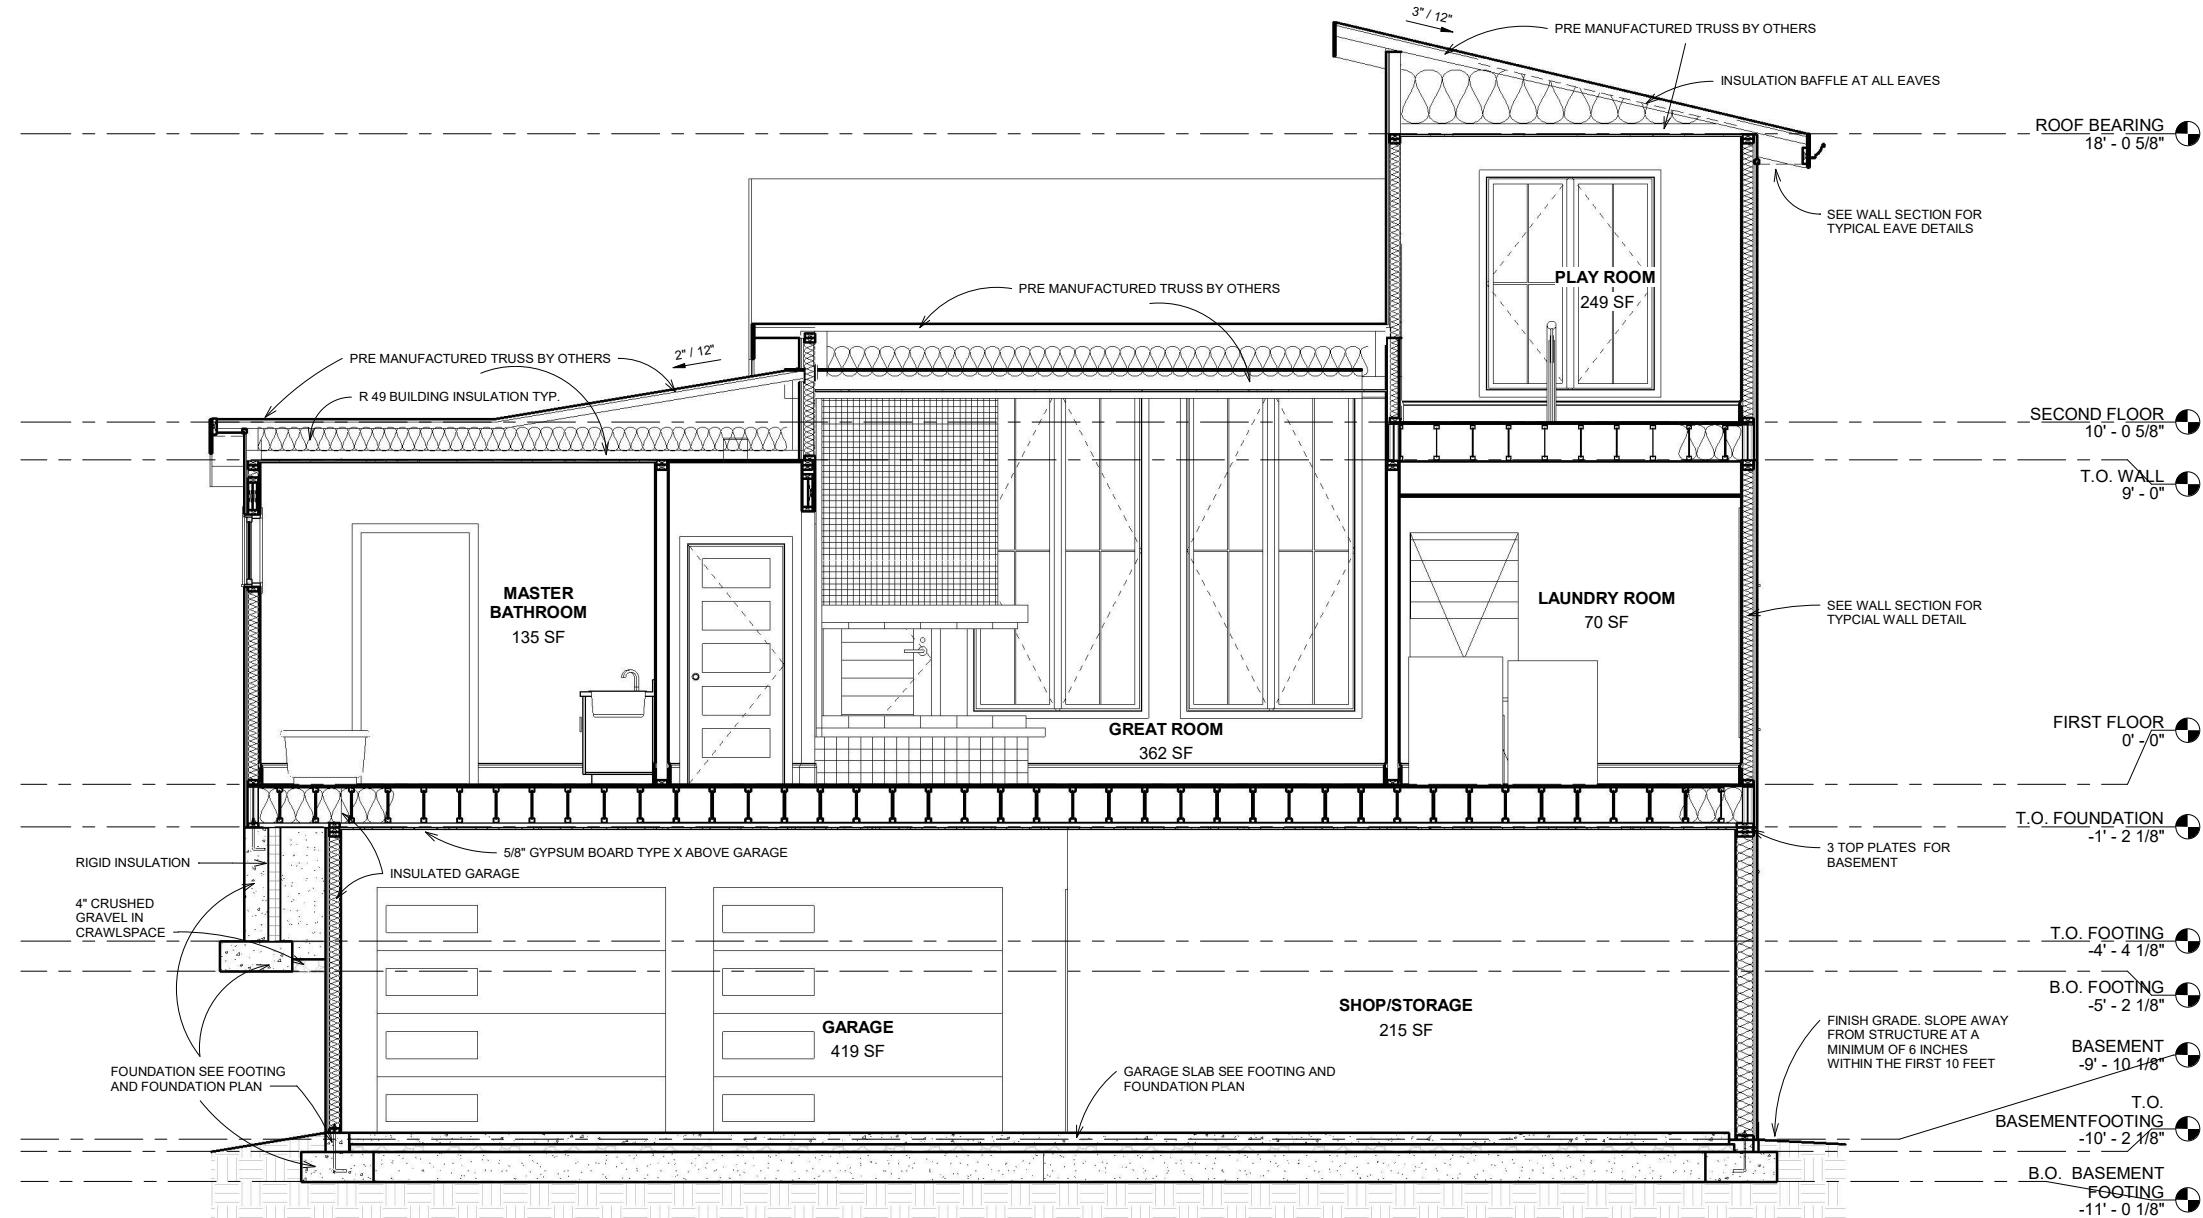

(1) BUILDING SECTION
3/8" = 1'-0"

PARKER HICKS MIDTERM HOUSE BUILDING SECTION

Project number	2022-001
Date	11/30/2022
Drawn by	PARKER HICKS
Checked by	CHECKER

A6


Scale

3/8" = 1'-0"



www.autodesk.com/revit

HALF SIZE

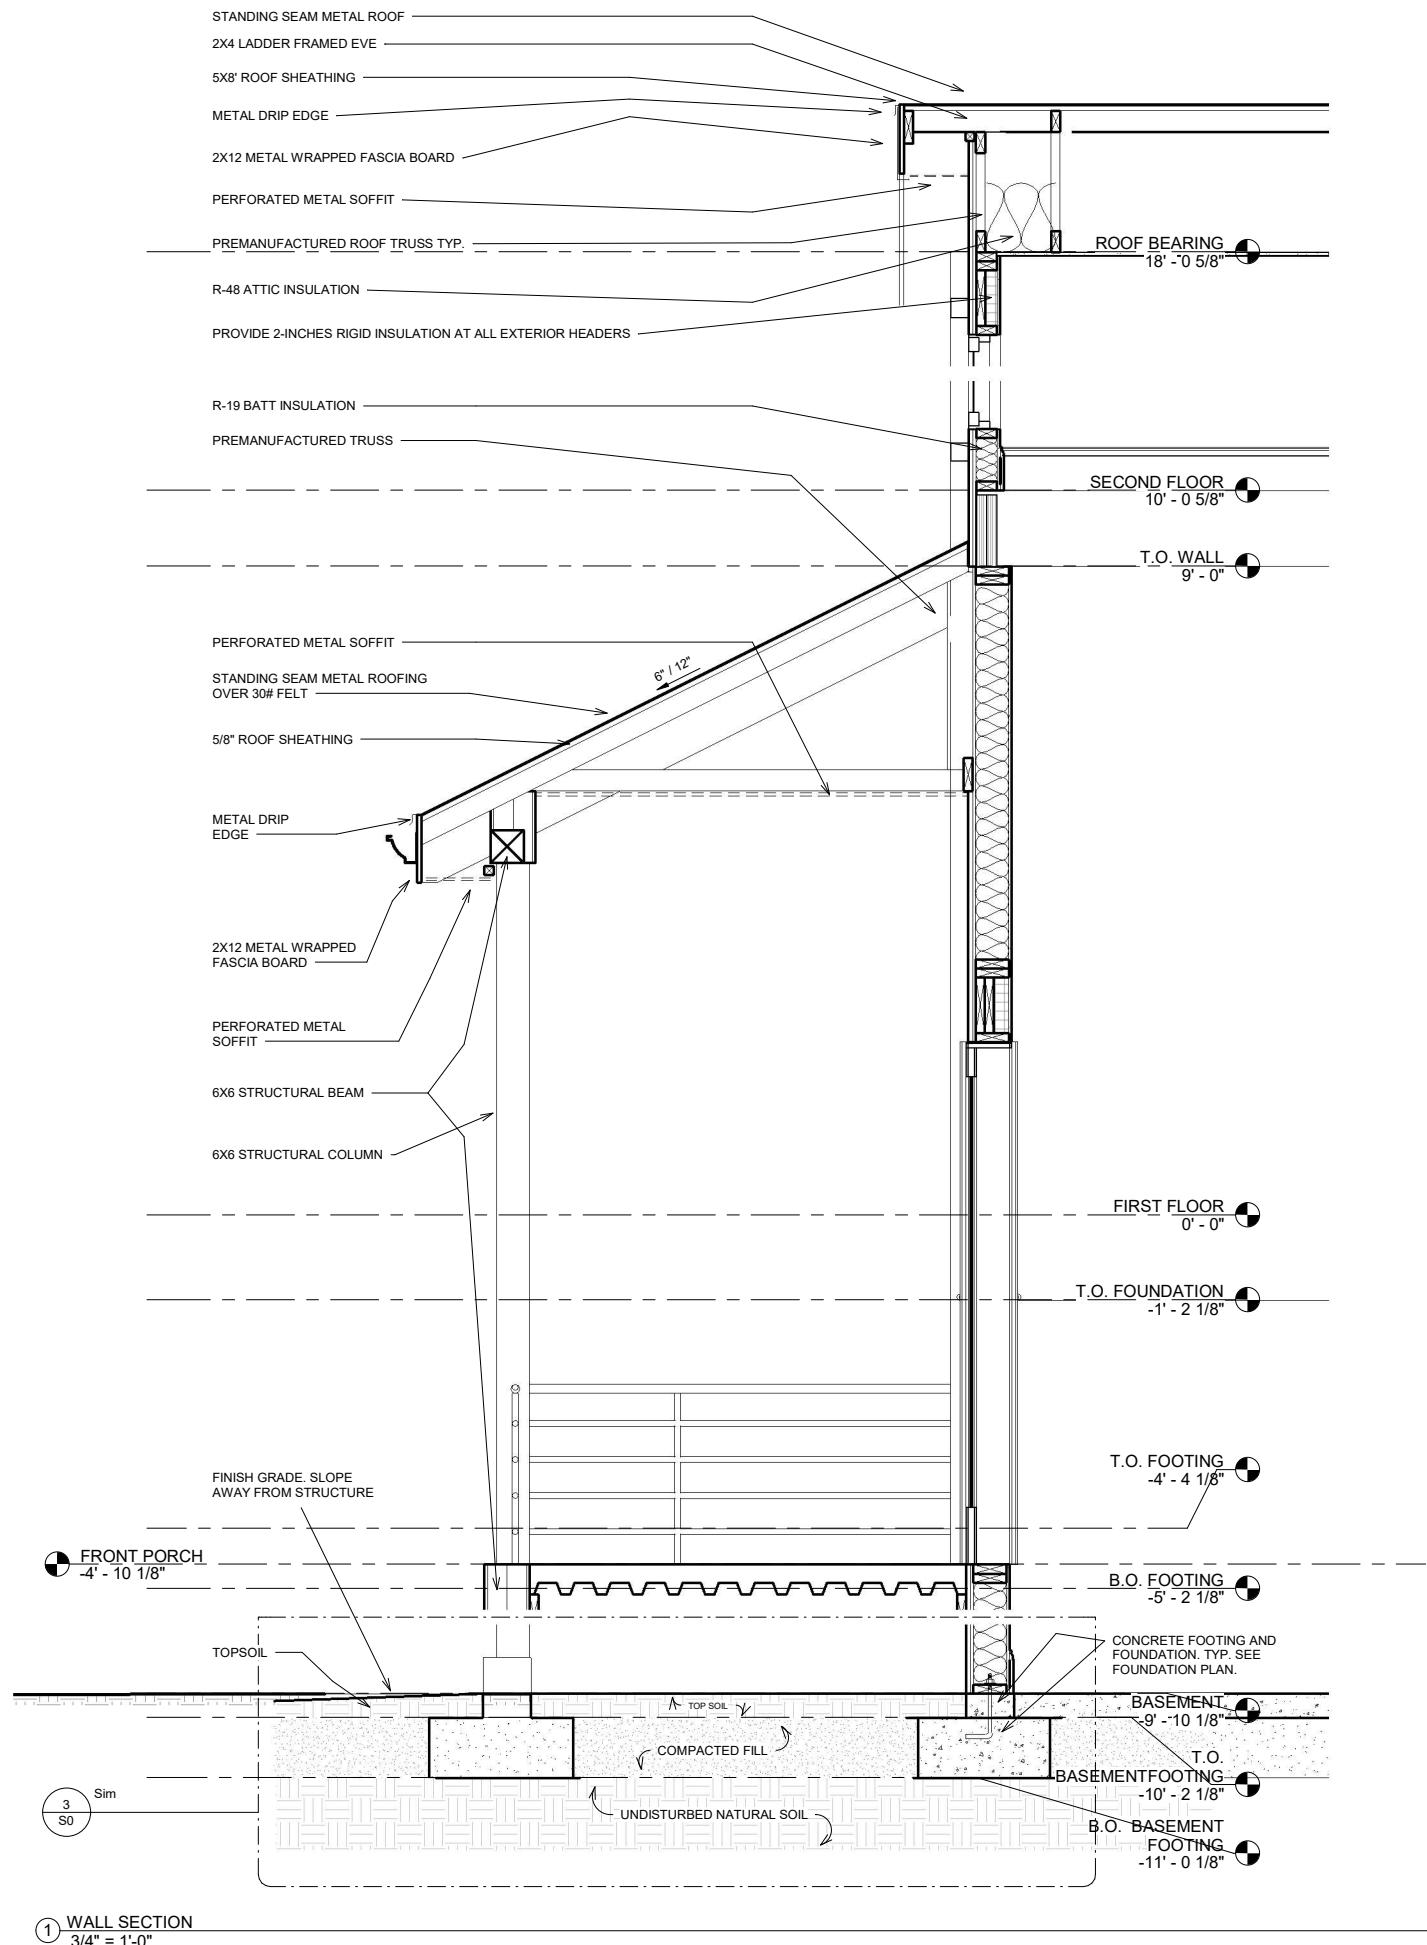

PARKER HICKS


MIDTERM HOUSE

WALL SECTION


Project number	2022-001
Date	11/30/2022
Drawn by	PARKER HICKS
Checked by	CHECKER

A7


3/4" = 1'-0"

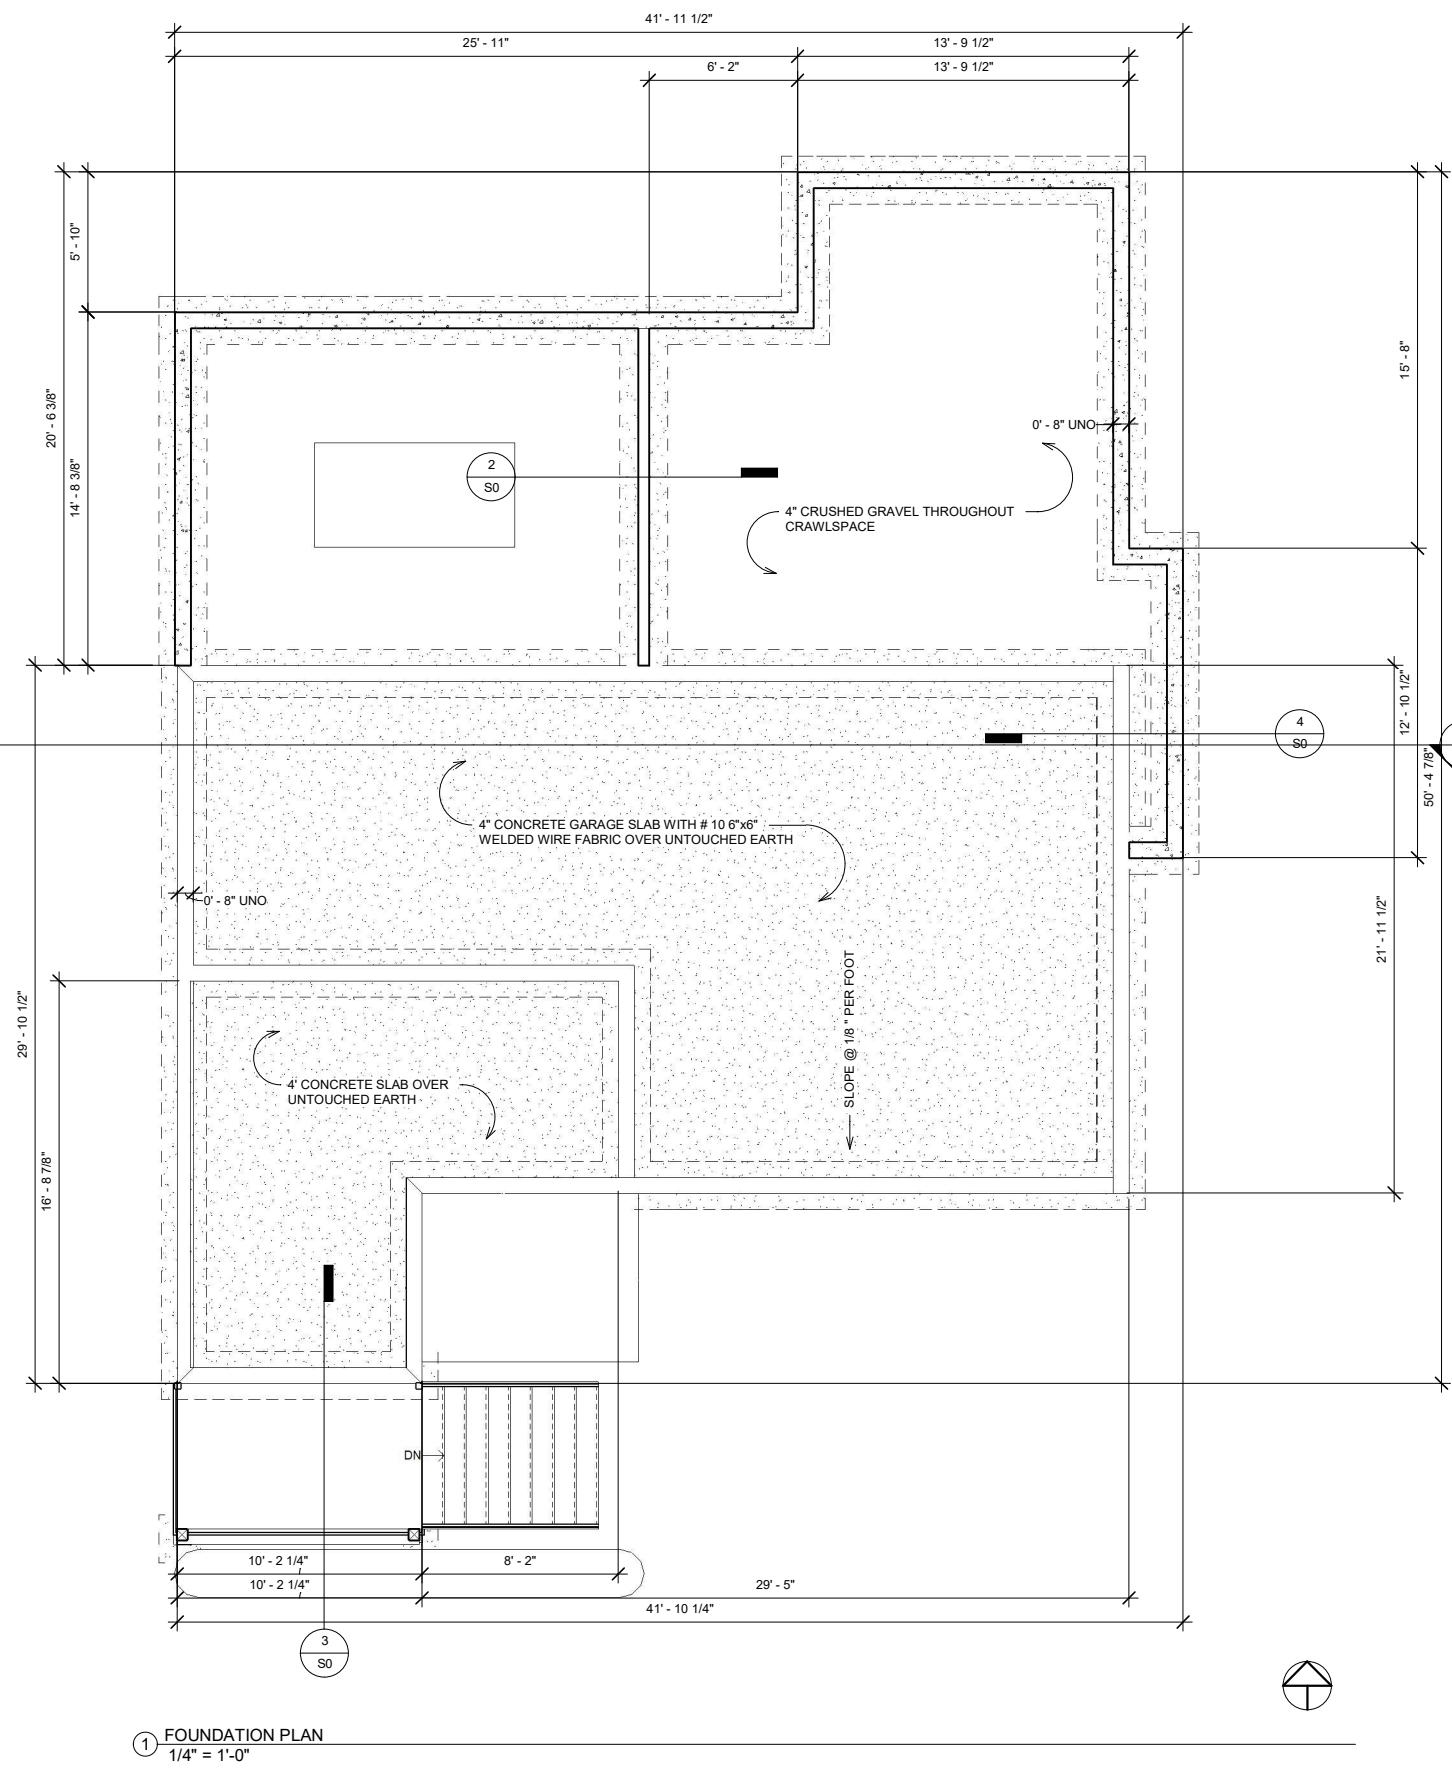


HALF SIZE

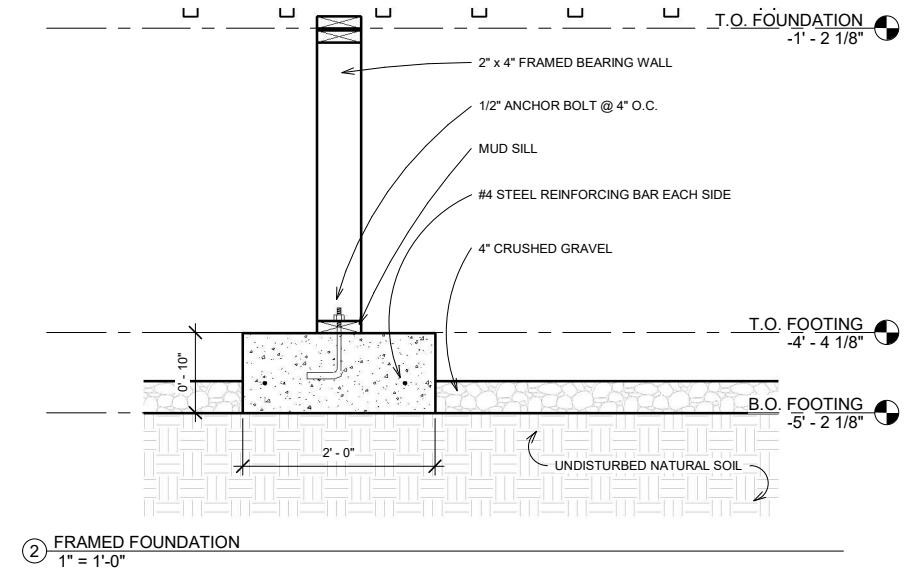

② FRAMED FOUNDATION

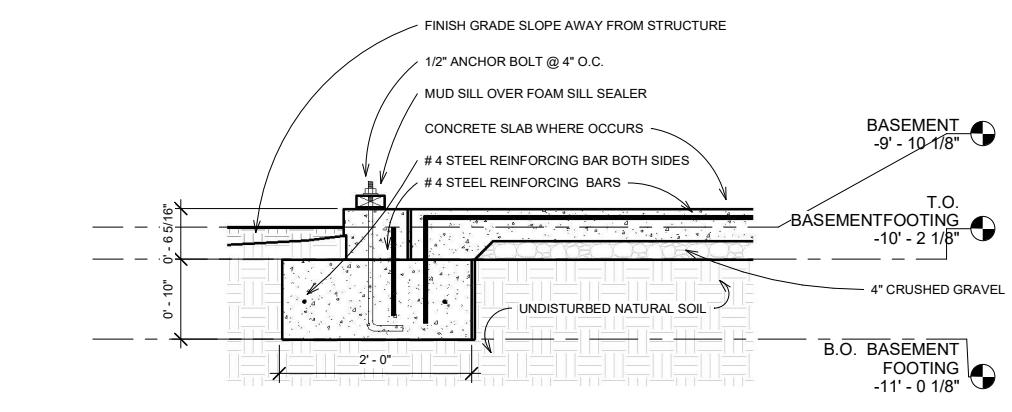

④ TYPICAL FOUNDATION
1" = 1'-0"

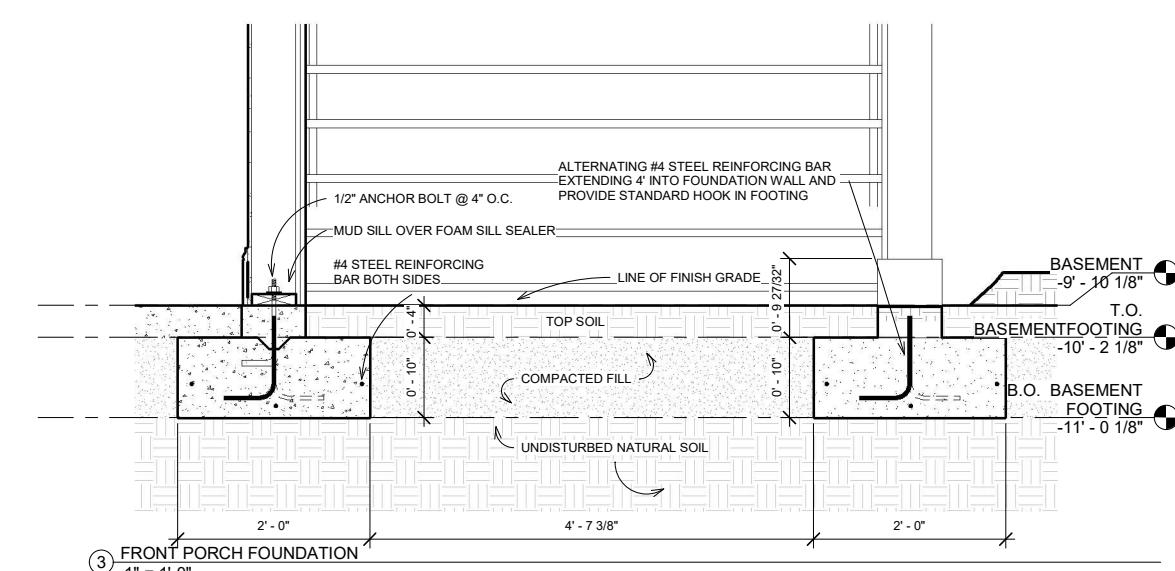

3 FRONT PORCH FOUNDATION
1" = 1'-0"

 AUTODESK®

www.autodesk.com/revit

Consultant
Address
Address
Phone
Fax
e-mail

PARKER HICKS
MIDTERM HOUSE
FOUNDATION PLAN

Project number	2022-001
Date	11/30/2022
Drawn by	PARKER HICKS
Checked by	T.A.

so

As indicated